
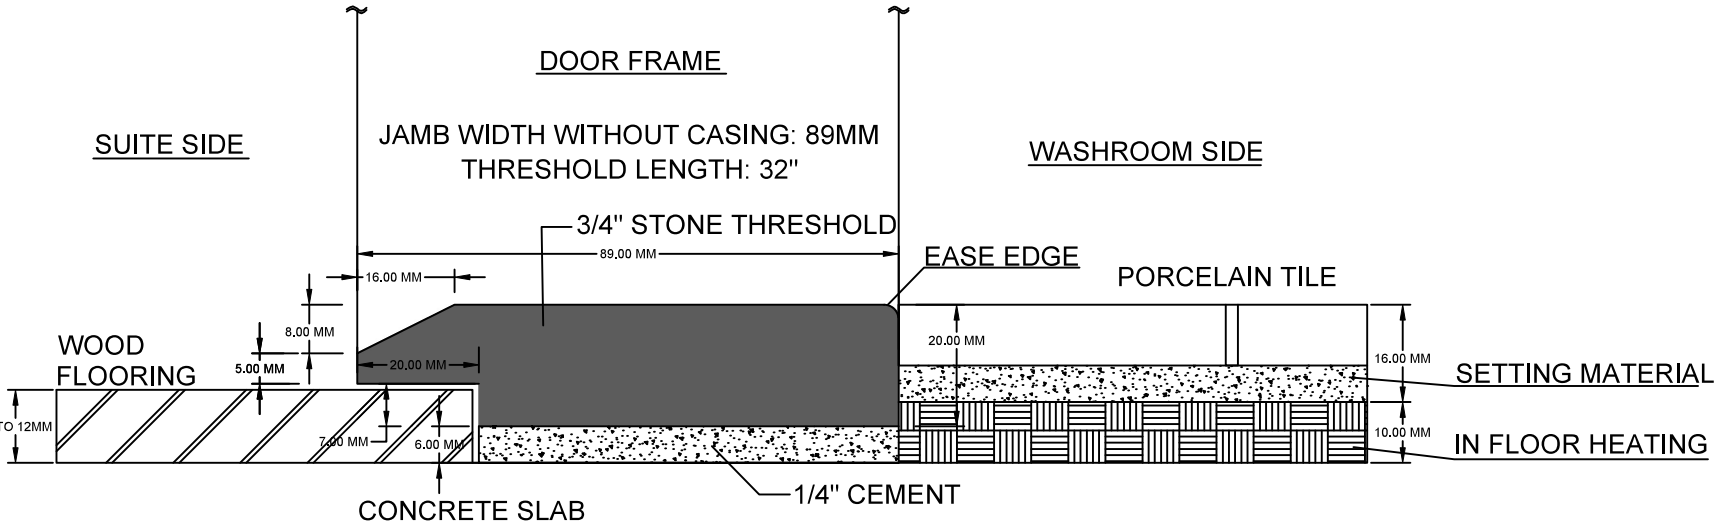


PLAN

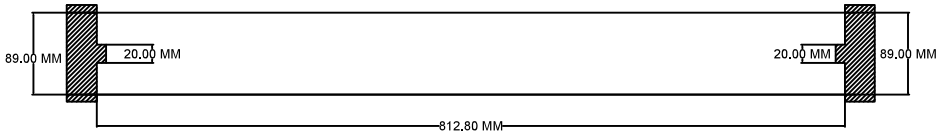

NOTES:
- SUITE 1906 ENSUITE WASHROOM FLOOR TO BE RAISED WITH LEVELING COMPOUND DUE TO CURBLESS SHOWER. THRESHOLD ONLY TO BE INSTALLED IN ENSUITE WASHROOM.
- SUITE 2005 INCLUDES IN-FLOOR HEATING MAT IN ENSUITE WASHROOM. THRESHOLD TO BE INSTALLED IN ENSUITE WASHROOM ONLY.
- SUITE 806, 1820, 1916, 2016, 2116, 2212, 2215, 2310, 2509, 2510, SPH02-W, SPH01-E, SPH02-E, SPH03-E, PH02-E IN-FLOOR HEATING TO BE INSTALLED IN MAIN AND ENSUITE WASHROOMS ONLY.

SUITE	SCHEME	THRESHOLD MATERIAL	COUNT
PH02-E	F	CEASARSTONE - QUARTZ ALPINE MIST NO. 5110	2
SPH01-E	H	CEASARSTONE - QUARTZ STATUARIO MAXIMUS NO. 5031	2
SPH02-E	G	CEASARSTONE - QUARTZ STATUARIO MAXIMUS NO. 5031	2
SPH02-W	H	CEASARSTONE - QUARTZ STATUARIO MAXIMUS NO. 5031	2
SPH03-E	F	CEASARSTONE - QUARTZ ALPINE MIST NO. 5110	2
806	F	CEASARSTONE - QUARTZ ALPINE MIST NO. 5110	2
1820	H	CEASARSTONE - QUARTZ STATUARIO MAXIMUS NO. 5031	2
1906	CUSTOM	**PLEASE CONFIRM**	1
1916	G	CEASARSTONE - QUARTZ STATUARIO MAXIMUS NO. 5031	2
2005	D	**PLEASE CONFIRM**	1
2016	H	CEASARSTONE - QUARTZ STATUARIO MAXIMUS NO. 5031	2
2116	G	CEASARSTONE - QUARTZ STATUARIO MAXIMUS NO. 5031	2
2212	F	CEASARSTONE - QUARTZ ALPINE MIST NO. 5110	2
2215	F	CEASARSTONE - QUARTZ ALPINE MIST NO. 5110	2
2310	H	CEASARSTONE - QUARTZ STATUARIO MAXIMUS NO. 5031	2
2509	F	CEASARSTONE - QUARTZ ALPINE MIST NO. 5110	2
2510	H	CEASARSTONE - QUARTZ STATUARIO MAXIMUS NO. 5031	2

KEY PLAN

FLOOR FINISHES LEGEND

FLOOR FINISHES NOTES

MATERIAL LEGEND

REV NO.	DATE	DESCRIPTION	DWG BY
4			
3			
2			
1	JULY 16th 2026		LH

PROJECT:

REF DRAWING NO:

SHOPDRAWING TITLE:

CROWN SUITES
WASHROOMS / LAUNDRY
THRESHOLD WITH
IN-FLOOR HEATING

Classic Tile Contractors Limited
1126 Northside Rd
Burlington, ON L7M 1H4
Tel 905 335 1700
Fax 905 335 1760

SHOP DRAWING NO: SD-02A

PROJECT NORTH